

Complete house plans / full roof access

A3 COORDINATED DESIGN REVIEW SET / THREE BEDROOMS, THREE ENSUITES / 08 SEPTEMBER 2026



FRONT

REAR

Full-stair roof option - refer to dimensioned drawings

DRAWING INDEX

- 01 Cover, index and design basis
- 02 Site, parking and main-floor area
- 03 Ground floor / built-in unit under the stair
- 04 First floor / roof-stair continuation
- 05 Roof plan / full-stair enclosure
- 06 Integrated front and rear elevations
- 07 Under-stair built-in / stair geometry locked
- 08 Developed stair profile and headroom
- 09 Roof setbacks and exit elevation
- 10 Original style references / context
- 11 Current exterior appearance

Print on A3 at 100% / actual size. Each drawing states its scale. Do not scale the photographs or the developed stair diagram horizontally.


This set replaces the separate compact-v4 and integrated-roof review PDFs. The current design includes full stairs to the roof.

FOR ARCHITECT / BUILDER REVIEW

Dimensioned vectors govern over the render. Measured site set-out, structural design, stair headroom, waterproofing, services and permit drawings remain to be coordinated by the project professionals.

A smaller footprint. More useful yard.

SITE STUDY / 1:100 AT A3 / ROOF ENCLOSURE ADDITIONAL: 9.02 m2 / 97.1 SQ FT

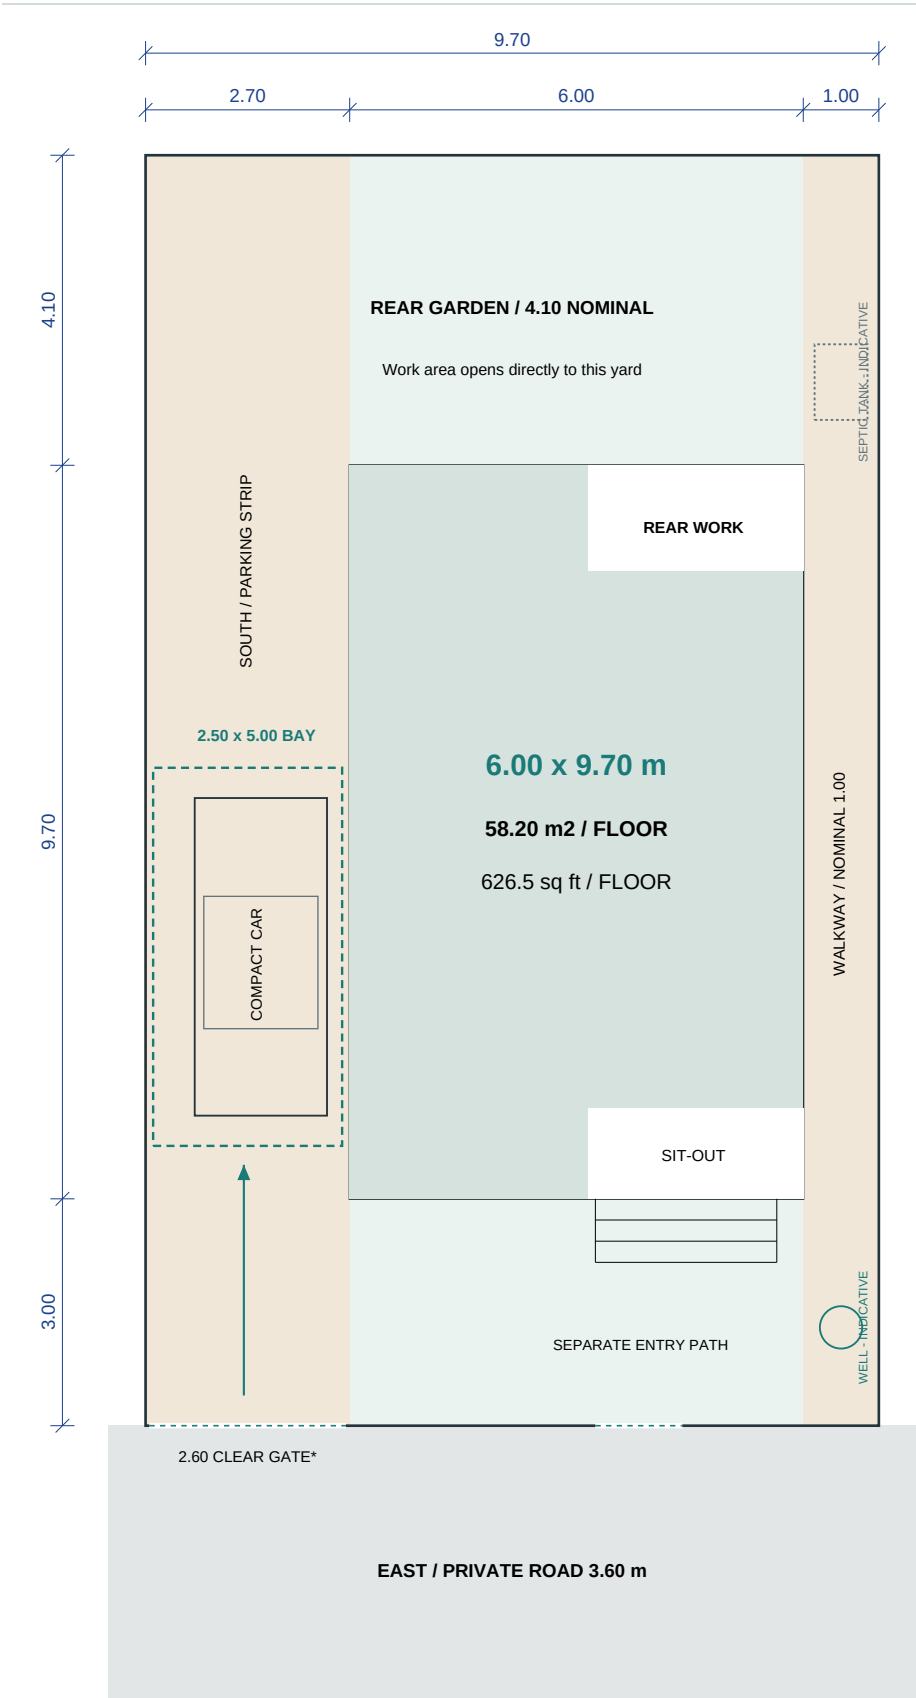

AREA LIMIT / COUNTED CONSERVATIVELY

Ground external envelope	58.20 m2 / 626.5 sq ft
First external envelope	58.20 m2 / 626.5 sq ft
Main floors only (roof additional)	116.40 m2 / 1,252.9 sq ft
Included on each floor	Walls, stairs + covered open spaces

SIDE PARKING - FITS AS A SPACE STUDY

A 2.50 x 5.00 m stall fits in the nominal 2.70 m south strip. The drawn car is 1.75 x 4.20 m without mirrors. This is for a compact car, with tight door clearance; no covered carport is added.

THE GATE IS THE UNRESOLVED PART

The 3.60 m road, boundary-wall thickness and actual vehicle turning circle control entry. The arrow shows approach only, not a verified swept path. Confirm with the real car and surveyed gate position; do not infer parking approval from this rectangle.

SOURCE PLOT IS SLIGHTLY SKEWED

The 4-cent plot sketch gives 9.70 m frontage/rear and side lengths 16.82 / 16.84 m, with 1.62 are stated area. This study uses a nominal 9.70 x 16.80 m rectangle. The separate old site plan has different geometry; a measured boundary overlay is needed before fixing yard clearances.

WALKWAY AND BUILDING EDGES


Keep the north path free of equipment and the south parking strip free of projecting fins or drains. Yard widths shown are nominal wall-to-boundary distances, not guaranteed finished clear widths. Front and rear steps sit in the yards.

INDICATIVE WELL AND SEPTIC POSITIONS

A well/borewell is marked in the northeast corner and a septic tank in the northwest corner, about 12.5 m apart along the plot depth. KPBR 2019 Rule 75 requires at least 7.5 m between any well and a septic tank or soak pit, plus 1.2 m from boundaries; this does not clear reliably across the 9.7 m width, only along the 16.8 m depth. Confirm exact points, and check for any neighbouring well within 7.5 m, with the panchayat engineer.

Ground floor / one built-in unit under the stair

R5 / 09 SEP 2026 / PLAN 1:55 AT A3 / STAIR AND APPROVED ARCHITECTURE UNCHANGED; ONE STORE-DOOR OPENING TO CONFIRM

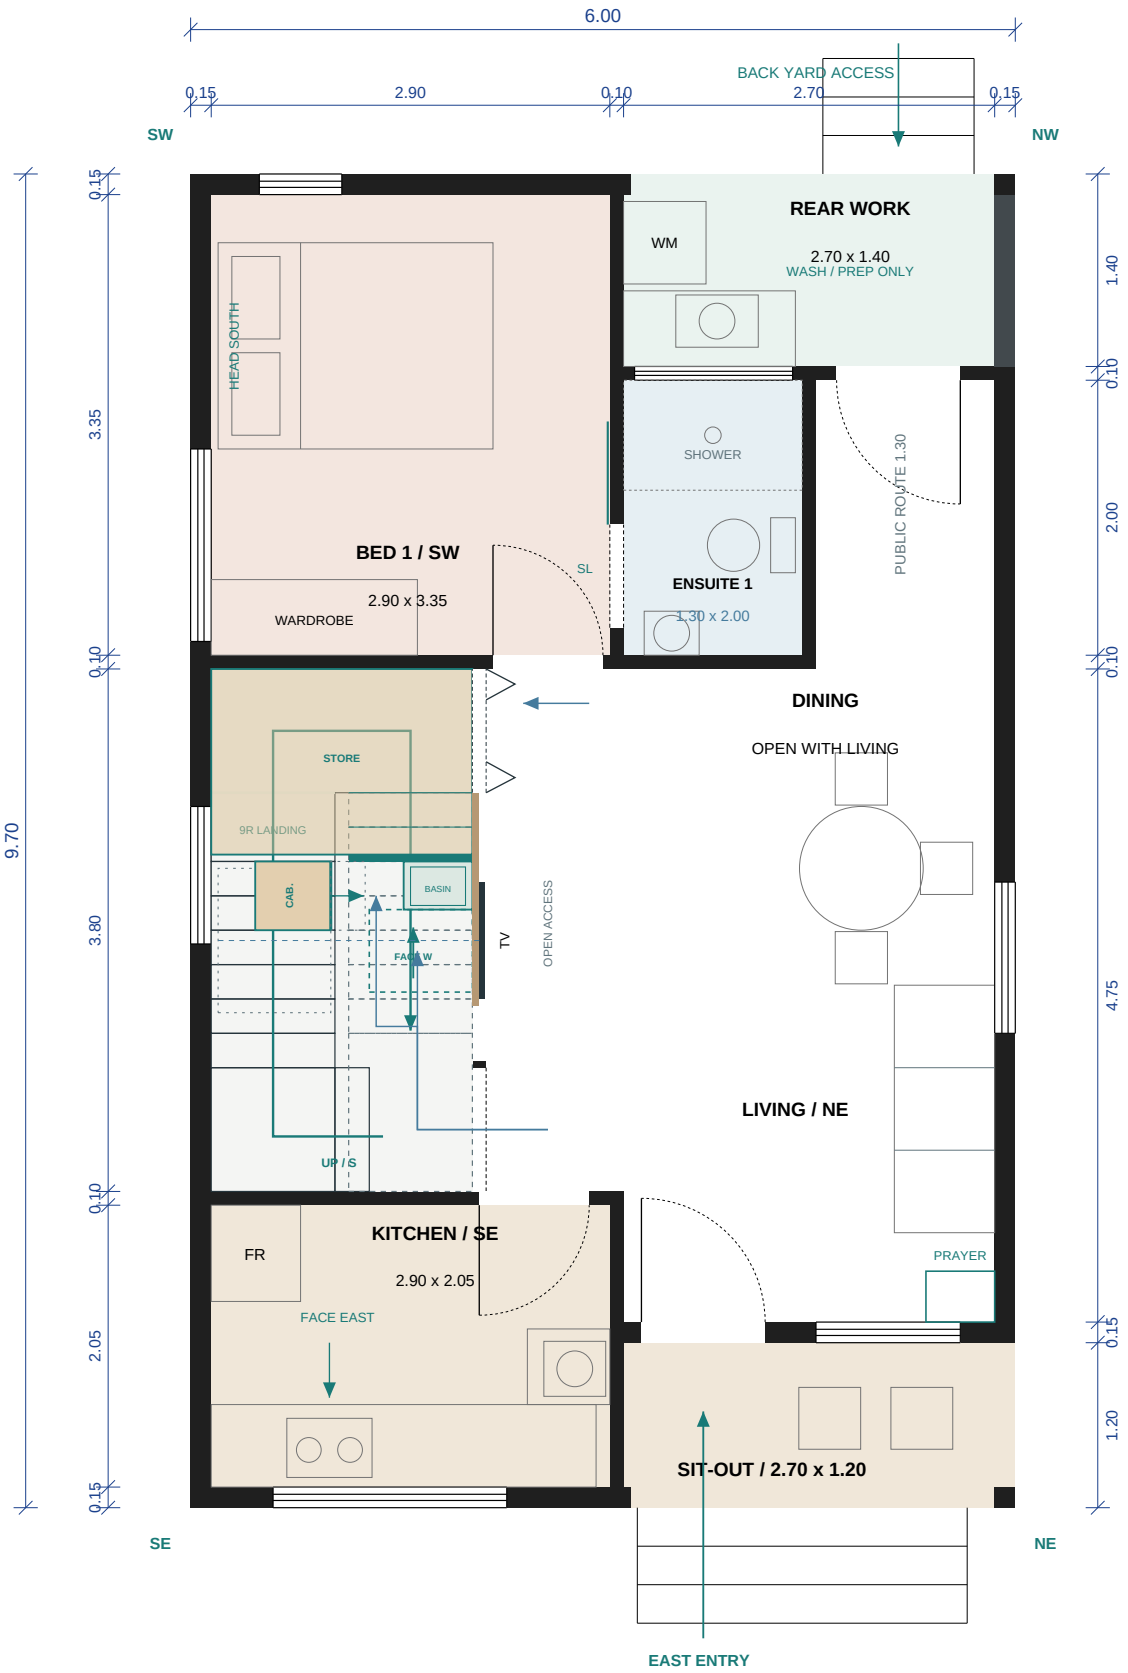

ONE BUILT-IN UNIT UNDER THE UPPER FLIGHT

Measured from the stair-side face of the bedroom wall: store 0-1.40 m, mirror partition at 1.40 m, semi-recessed basin 1.40-1.75 m, standing zone 1.75-2.35 m. The 1.47 m-high zone under the landing is no longer empty; the person stands only where the soffit is 2.17 m or higher.

UNDER-LANDING STORE

1.90 x 1.35 m floor, about 2.6 m² and 3.7 m³, with a stepped carcass top 1.42 m under the landing rising to 1.59 and 1.77 m under risers 10 and 11. Two 450 mm bifold leaves, 1.40 m high, open from the passage beside the bedroom door, where the user stands under the full 2.85 m slab. The pocket under the lower landing is crouch-in bulk storage.

WEST-FACING BASIN, SHIFTED ONLY AS FAR AS NEEDED

500 x 350 mm basin on a 350 mm counter with a drawer; rim +0.86 m; front edge 1.75 m from the wall, 0.53 m closer than R4. Mirror on the partition, top +1.75 m under the 1.82 m soffit; 2.00 m over the bowl. Standing zone 750 x 600 mm: 2.17 m over the 150 mm leaning strip, 2.35 m over the body line, 2.53 m at the rear.

CABINET, CLOSING PANEL AND TV

The 500 x 550 x 1080 mm cabinet stays under the last two lower-flight treads; its doors are now reached from the wash side through a 400 mm strip beside the basin under a 2.00-2.17 m soffit (stoop access). The former 600 mm passage opening closes with a fixed oak panel on the TV line. TV unchanged at y = 4.125 m, screen centre +1.10 m.

ROUTES AND HEADROOM BASIS

Basin: through the existing 900 mm stair entry, turning behind the TV panel. Store: from the passage face. Cabinet: past the basin. Blue arrows show the routes; the dashed old-storage outline is the TV reference only. Headroom uses the modeled 120 mm stair zone; a thicker waist slab reduces each figure by the difference. Fallback: basin front at 2.00 m keeps 2.35 m throughout.

ONE WALL OPENING / ARCHITECTURE OTHERWISE LOCKED

The only architectural change is a 900 x 1400 mm store opening in the retained 100 mm stair-side partition at y = 5.20-6.10 m; the wall above remains. The structural engineer must confirm the intermediate landing does not bear on it; fallback is a mirror-fronted door with no wall change. Stair, both landings, upper flight, kitchen, bedroom and all other walls, doors and windows keep their R2 geometry.

First floor / two bedrooms, two ensuites

DIMENSIONED PLAN / 1:55 AT A3 / TWO BEDROOMS, TWO ENSUITES, STUDY AND BALCONIES



FRONT MATCHES THE REFERENCE

The left window belongs to the study/family space. The front balcony is on the right, over the ground-floor sit-out, with a recessed sliding door and glass railing.

BEDROOMS IN SW AND NORTH

The southwest master retains 2.90 x 3.35 m clear dimensions. The north bedroom is now a full 2.70 x 3.60 m rectangle (9.72 m²). Each bedroom has its own door directly into its own 1.30 x 2.00 m ensuite.

NO BEDROOM IN THE SOUTHEAST

The southeast front room is a study/family space above the kitchen. The child's bedroom is in the north band. The master stays southwest, with southward bed-head orientation.

REAR DRYING TERRACE

The covered rear balcony remains above the work area. Access is now through a side door from the master bedroom, not through either ensuite. It is private to the master; the front balcony remains accessible from the common gallery.

TWO SEPARATE ENSUITES


Ensuite 2 serves only the master and stacks above Ensuite 1. Ensuite 3 serves only Bedroom 3 and sits above the ground service passage, not a bedroom or kitchen. The two bathrooms are separated by a full-height wall. The south stair continues to the roof; see sheets 05 and 08 for roof access.

AREA AND STRUCTURE

The whole first-floor envelope is counted at 58.20 m², including the stair opening and both covered balconies. Columns, beams, slab thickness and wet-area waterproofing must be engineered without reducing the shown clear routes.

Roof access / one compact enclosure

ROOF PLAN 1:55 AT A3 / FULL SOUTH STAIR / FRONT AND REAR FACADES RETAINED

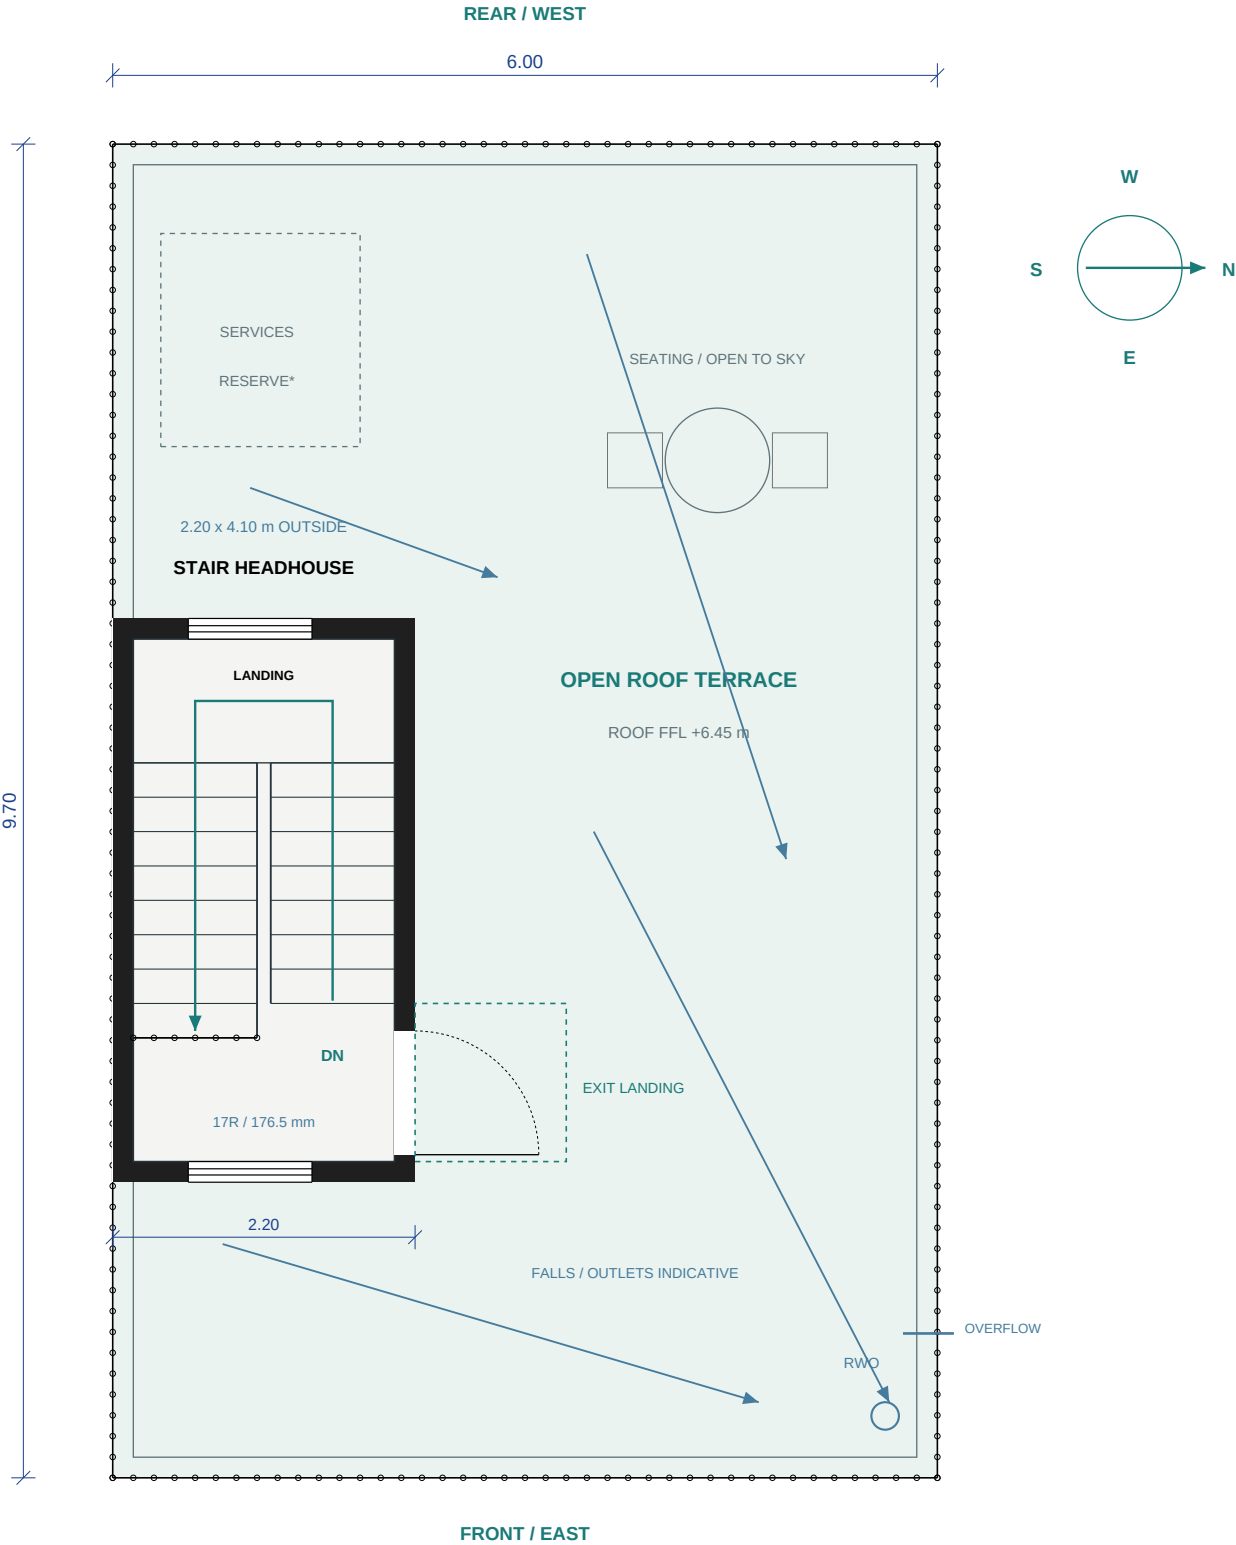

MATERIALS CONNECT THE TWO ROOF LEVELS

Use vertical timber-look cladding on the enclosure's east and west end walls to match the existing screen. Warm-white side walls and a shallow white fascia with a thin charcoal edge keep the upper enclosure visually light.

SAME STAIR, SAME FOOTPRINT

The roof enclosure remains 2.20 x 4.10 m outside, adding 9.02 m² / 97.1 sq ft. Its front face is set back 2.15 m; the rear face is set back 3.45 m. Ground and first floors remain 626.5 sq ft each.

KEEP THE OPEN ROOF USABLE

The 900 mm exit door opens onto the north-side roof landing. Keep its swing and approach clear. The perimeter guard is shown continuously at 1.10 m concept height; final infill and fixings need detailed design.

THE SILHOUETTE IS TALLER

The cap is +9.00 m, 1.60 m above the existing +7.40 m timber screen. The enclosure is narrower and set back, but remains visible. This option retains the approved first-floor rear canopy and toilet-vent arrangement.

DETAILING STILL TO COORDINATE

Cladding build-up must fit the stated envelope. Coordinate weathering, cap flashings, waterproofing, guard anchors, stair structure and clear headroom. Drainage arrows and the services reserve are inherited concept indications, not installation details.

A stepped roofline in the same materials


FRONT / REAR ELEVATIONS 1:55 AT A3 / FULL PROJECTED HEIGHTS, WITHOUT PERSPECTIVE CONCEALMENT

FRONT / EAST



The narrow timber-clad enclosure rises behind the existing front-left screen. Repeat its white cap and dark edge; retain the front balcony, windows and entrance below.


REAR / WEST

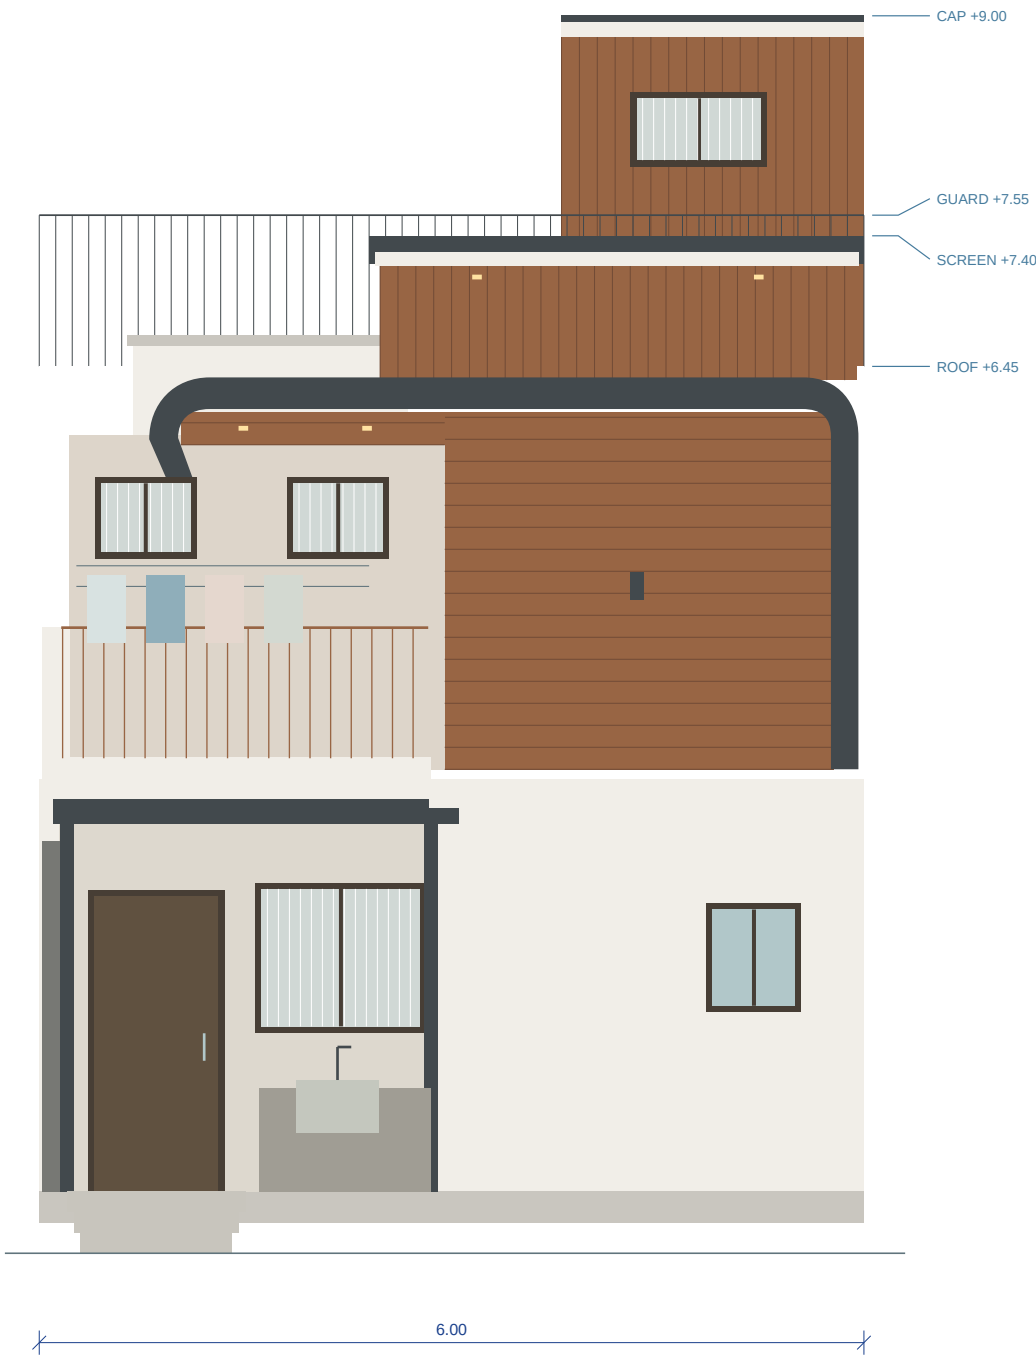

At the rear the enclosure sits behind the right timber screen. The open left drying balcony, short curved canopy return, two toilet vents and concealed master side entry remain.

Under-stair built-in / stair geometry locked

R5 / 09 SEP 2026 / STAIR PLAN 1:25 AND BAY SECTION 1:40 AT A3 / PROFILES ARE DIAGRAMMATIC

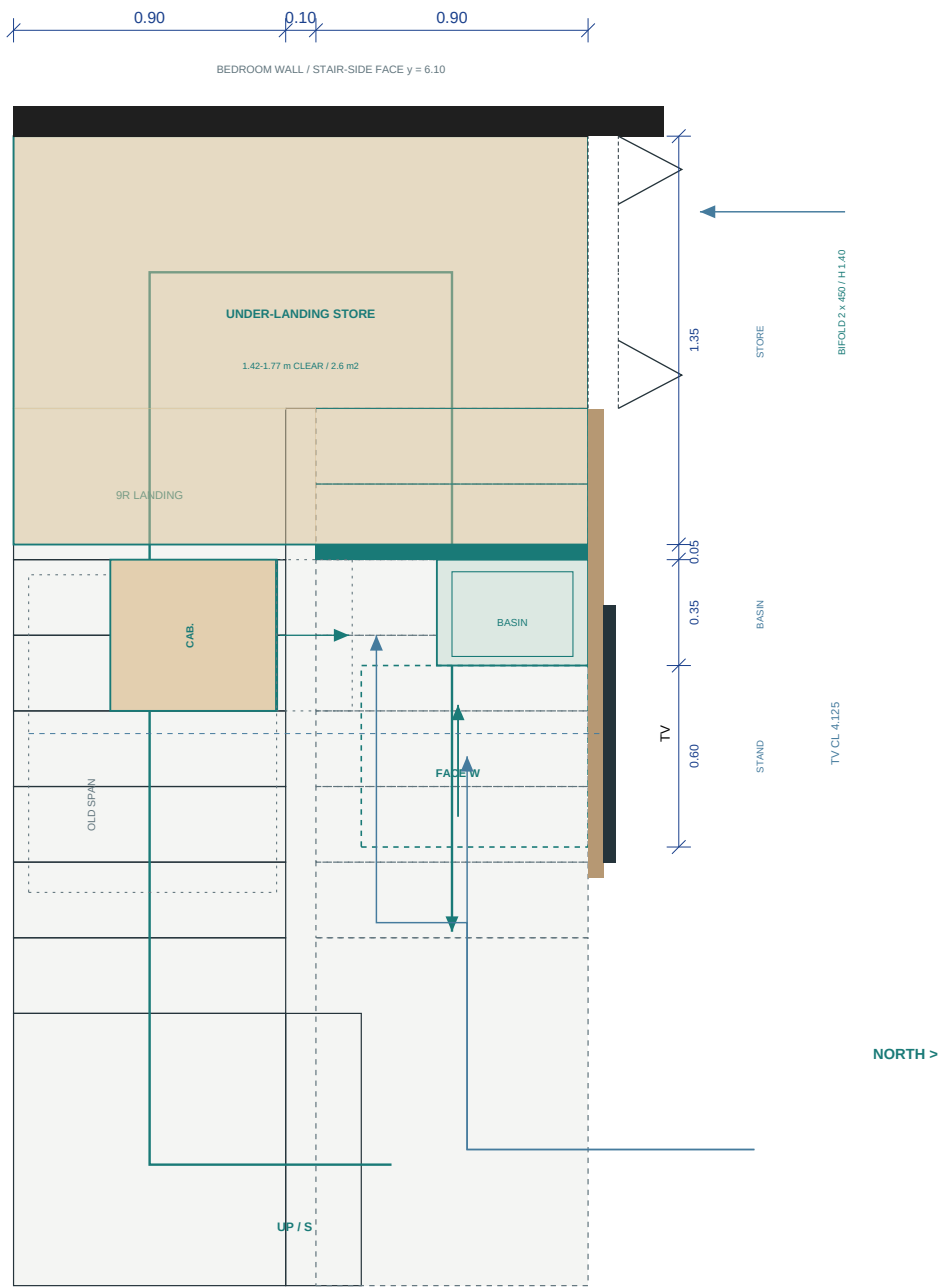

One built-in unit: store, mirror partition, basin

Distances are measured from the stair-side face of the bedroom wall: store 0-1.40 m, mirror partition at 1.40 m, basin 1.40-1.75 m, standing zone 1.75-2.35 m. Blue arrows: basin route from the stair entry, cabinet route beside the basin, store doors from the passage.

1 / UNDER-LANDING STORE, 0-1.40 m FROM THE BEDROOM WALL

Floor 1.90 x 1.35 m (about 2.6 m2 and 3.7 m3, against 0.3 m3 in the cabinet) beneath the intermediate landing, its 500 mm extension and risers 10-11. Carcass top 1.42 m under the landing, stepping to 1.59 and 1.77 m under the flight, 45-55 mm below each soffit. Two 450 mm bifold leaves, 1.40 m high, open from the passage beside the bedroom door under the full 2.85 m slab; the pocket under the lower landing is crouch-in bulk storage.

2 / STEPPED VANITY, USER FACES WEST

Mirror partition at 1.40 m, top +1.75 m under the 1.82 m soffit. 500 x 350 mm semi-recessed basin on a 350 mm counter with a drawer, rim +0.86 m, front edge 1.75 m from the wall: 0.53 m closer than R4 and the westernmost usable line. Standing zone 750 x 600 mm at 1.75-2.35 m: 2.17 m over the 150 mm leaning strip (30 mm under the 2.20 m benchmark, disclosed), 2.35 m over the body line, 2.53 m at the rear; 2.00 m over the bowl. Fallback: front edge at 2.00 m keeps 2.35 m.


3 / CABINET, CLOSING PANEL AND TV

The 500 W x 550 D x 1080 H mm cabinet stays under the last two lower-flight treads at y = 4.20-4.70 m. Its doors are now reached from the wash side through a 400 mm strip beside the basin under a 2.00-2.17 m soffit: stoop access to a low cabinet, not a passage. The former 600 mm passage opening at y = 4.60-5.20 m closes with a fixed 50 mm oak panel, 1.70 m high, on the TV line. TV unchanged: centreline y = 4.125 m, screen +0.785 to +1.415 m, 950 x 50 x 1700 mm backing at x = 2.05-2.10 m.


4 / THE ONE WALL OPENING / EVERYTHING ELSE LOCKED

The store door is a 900 x 1400 mm opening in the retained 100 mm stair-side partition at y = 5.20-6.10 m; the wall above the head remains. The structural engineer must confirm that the intermediate landing does not bear on this partition before it is cut. Fallback: a mirror-fronted door on the partition and a crouch-in cupboard from the wash side, with no wall change. Everything else keeps its exact R2 geometry: stair, landings, kitchen, bedroom, walls, doors and windows.

SECTION ALONG THE UPPER-FLIGHT BAY / LOOKING SOUTH / 1:40

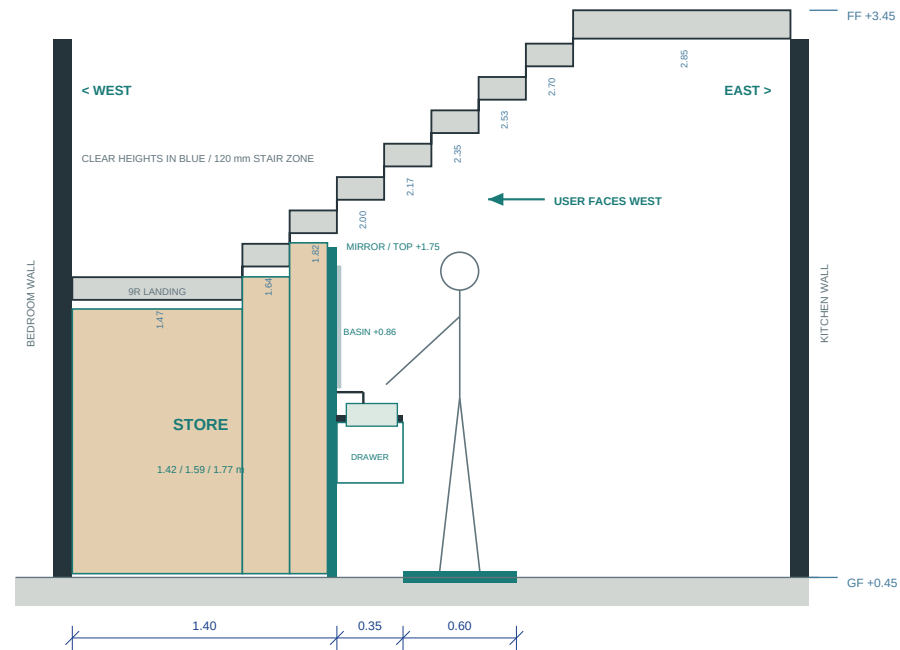


LOWER FLIGHT / CABINET RETAINED

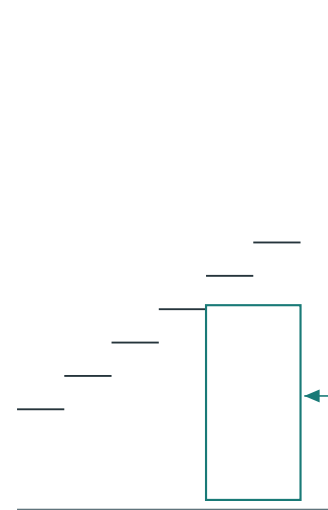

500 x 550 x 1080 mm under treads 7-8; doors face the wash side.

First-floor stair and roof headroom


PROPOSED FIRST-FLOOR STAIR 1:35 / DEVELOPED STAIR PROFILE 1:50 AT A3

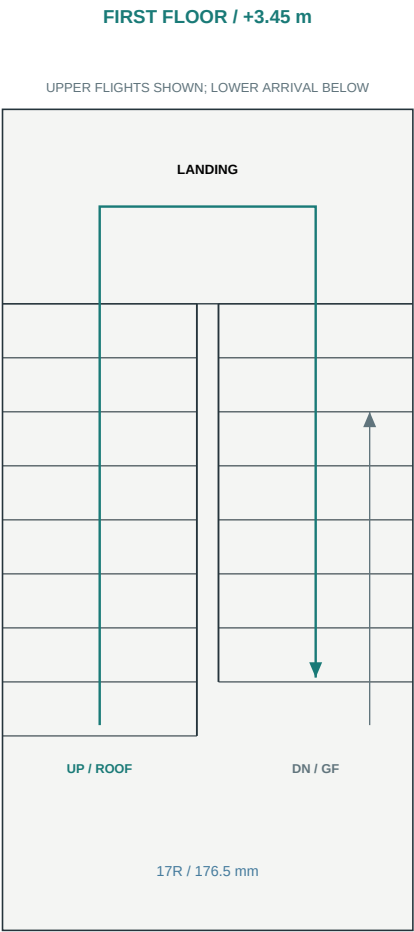

Remove the former guard across the bottom of the upward flight at first-floor level. The north return flight lands from below; the south flight begins the next rise to the roof.

Two rises of 3.00 m: GF to FF, then FF to roof. Each storey has 17 equal risers of 176.47 mm, 250 mm treads and 900 mm clear flights/landing. Structural stair thickness and all walking-line headroom still require verification.

The existing +7.40 m decorative screen is too low to be a roof-access enclosure. The new stair cover is +9.00 m, set back 2.15 m from the front and 3.45 m from the rear. Setbacks reduce visibility; they do not guarantee an unchanged roof silhouette.

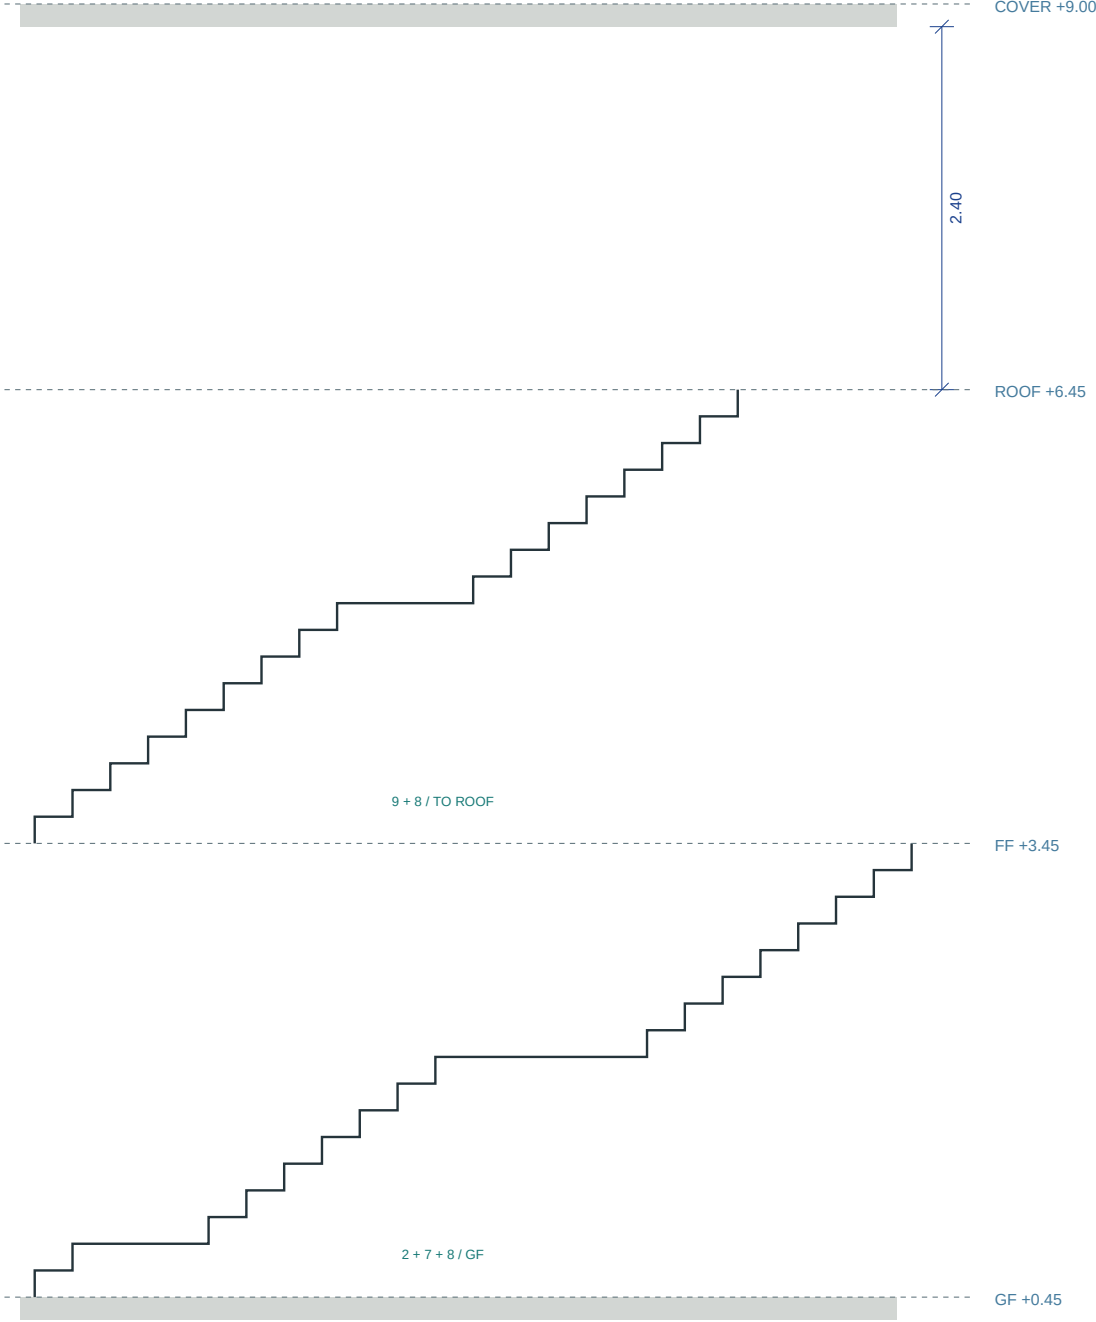


UNFOLDED PATHS / NOT HORIZONTAL SET-OUT

R2 developed paths: GF has a 2 + 7 + 8-riser turn; first-to-roof retains 9 + 8. The GF upper flight and first-floor connection are fixed. Do not set out horizontal building dimensions from this diagram.

Setbacks, height and the roof exit

LONGITUDINAL MASSING PROFILE 1:50 / ENCLOSURE NORTH ELEVATION 1:35 AT A3

SOUTH-WING PROFILE / FRONT AT LEFT

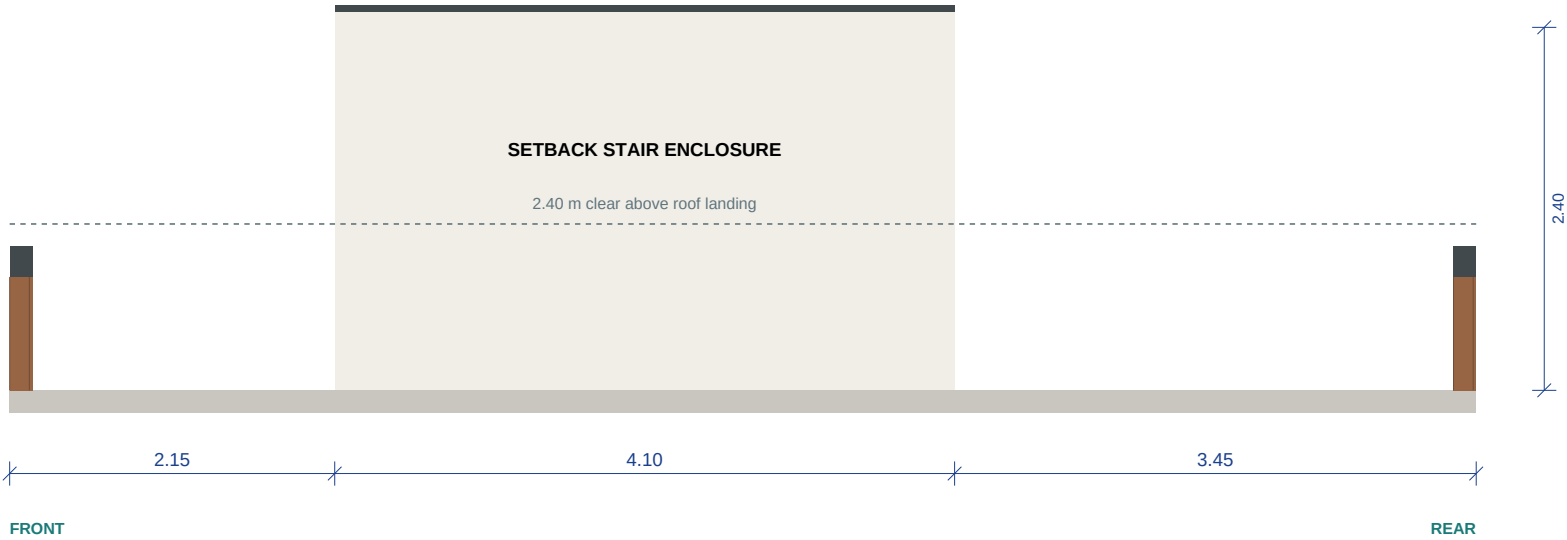

The foreground screens stay at +7.40 m. The new cap is +9.00 m; the dashed guard top is +7.55 m. The long enclosure wall uses warm-white plaster. Screen thickness is diagrammatic; this is a massing profile, not a stair section.


FULL STAIR GEOMETRY RETAINED

Continue the south dog-leg stair for another 3.00 m rise: 17 equal risers of 176.47 mm, 250 mm treads, and 900 mm clear flights and landing. See sheet 08 in this set for the developed stair profile.

HEIGHT AND AREA ARE EXPLICIT

Cap +9.00 m; roof landing +6.45 m; underside +8.85 m. Added enclosure 9.02 m²; conservative combined enclosed/covered study area 125.42 m² / 1,350.0 sq ft. Finishes do not enlarge the proposed enclosure.

ROOF EXIT / NORTH SIDE

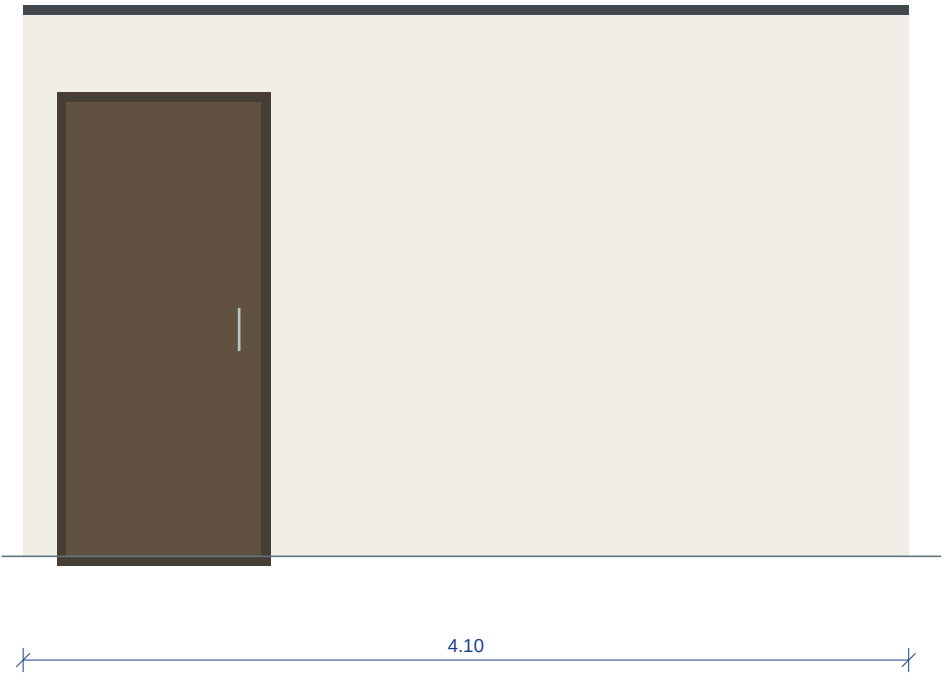

The door sits near the front end of the north wall and opens outward onto the roof. It is distinct from the master-bedroom balcony door one floor below. Confirm the finished threshold and landing drainage together.

Original style references / design context

REFERENCE IMAGES ONLY / NOT THE CURRENT OPENING ARRANGEMENT OR ROOF HEIGHT / NOT TO SCALE

ORIGINAL FRONT REFERENCE



Style source: white plaster, timber, rounded charcoal surrounds and recessed balconies. The current design adds the taller setback roof-stair enclosure and continuous roof guarding shown on sheets 05, 06, 09 and 11.

ORIGINAL REAR REFERENCE



The original rear photo shows superseded doors and an outdoor hearth. Current rear openings follow the plans: an independent ground service route, two upper toilet vents, master-bedroom side balcony entry, and a wash-only work area.

Current exterior / full roof access

PHOTOREALISTIC APPEARANCE STUDY / NOT TO SCALE / DIMENSIONED PLANS AND ELEVATIONS GOVERN



FRONT



REAR

Full-stair roof option - refer to dimensioned drawings

The stair enclosure has matching timber end walls, warm-white sides and a white/charcoal cap. It rises 1.60 m above the existing screen. Two toilet vents replace the former upper rear door; the master balcony entrance remains on the side.